



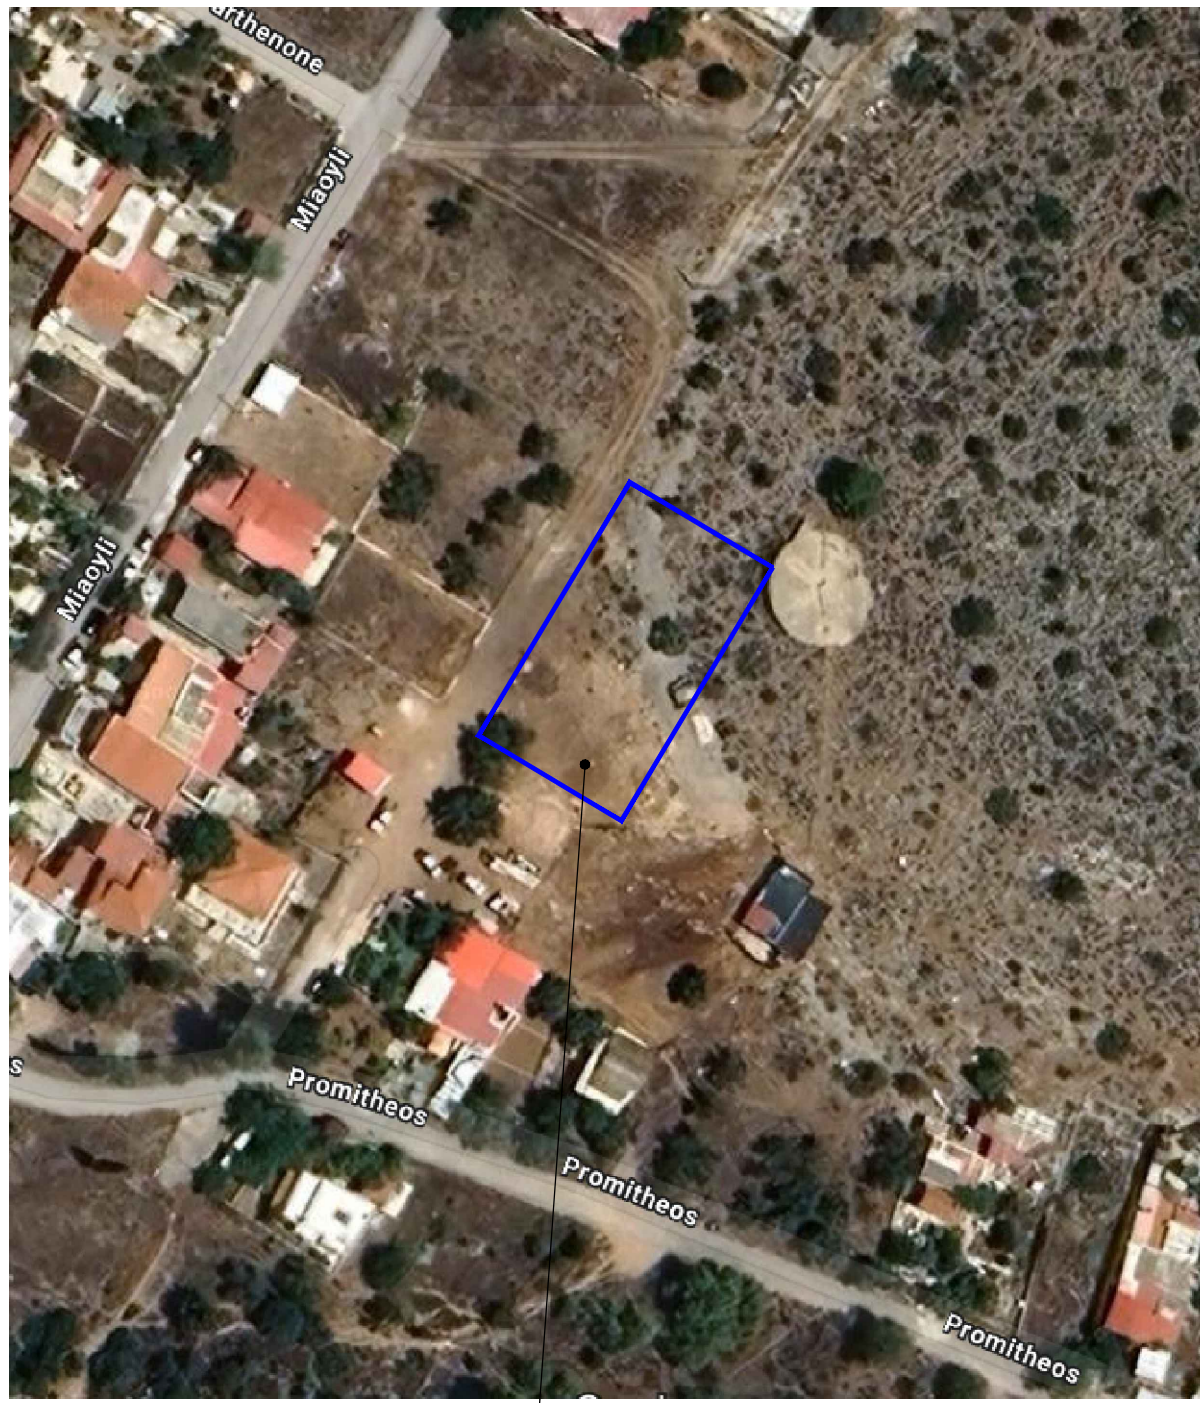

ΔΟΥΡΟΦΟΡΙΚΗ ΛΗΨΗ

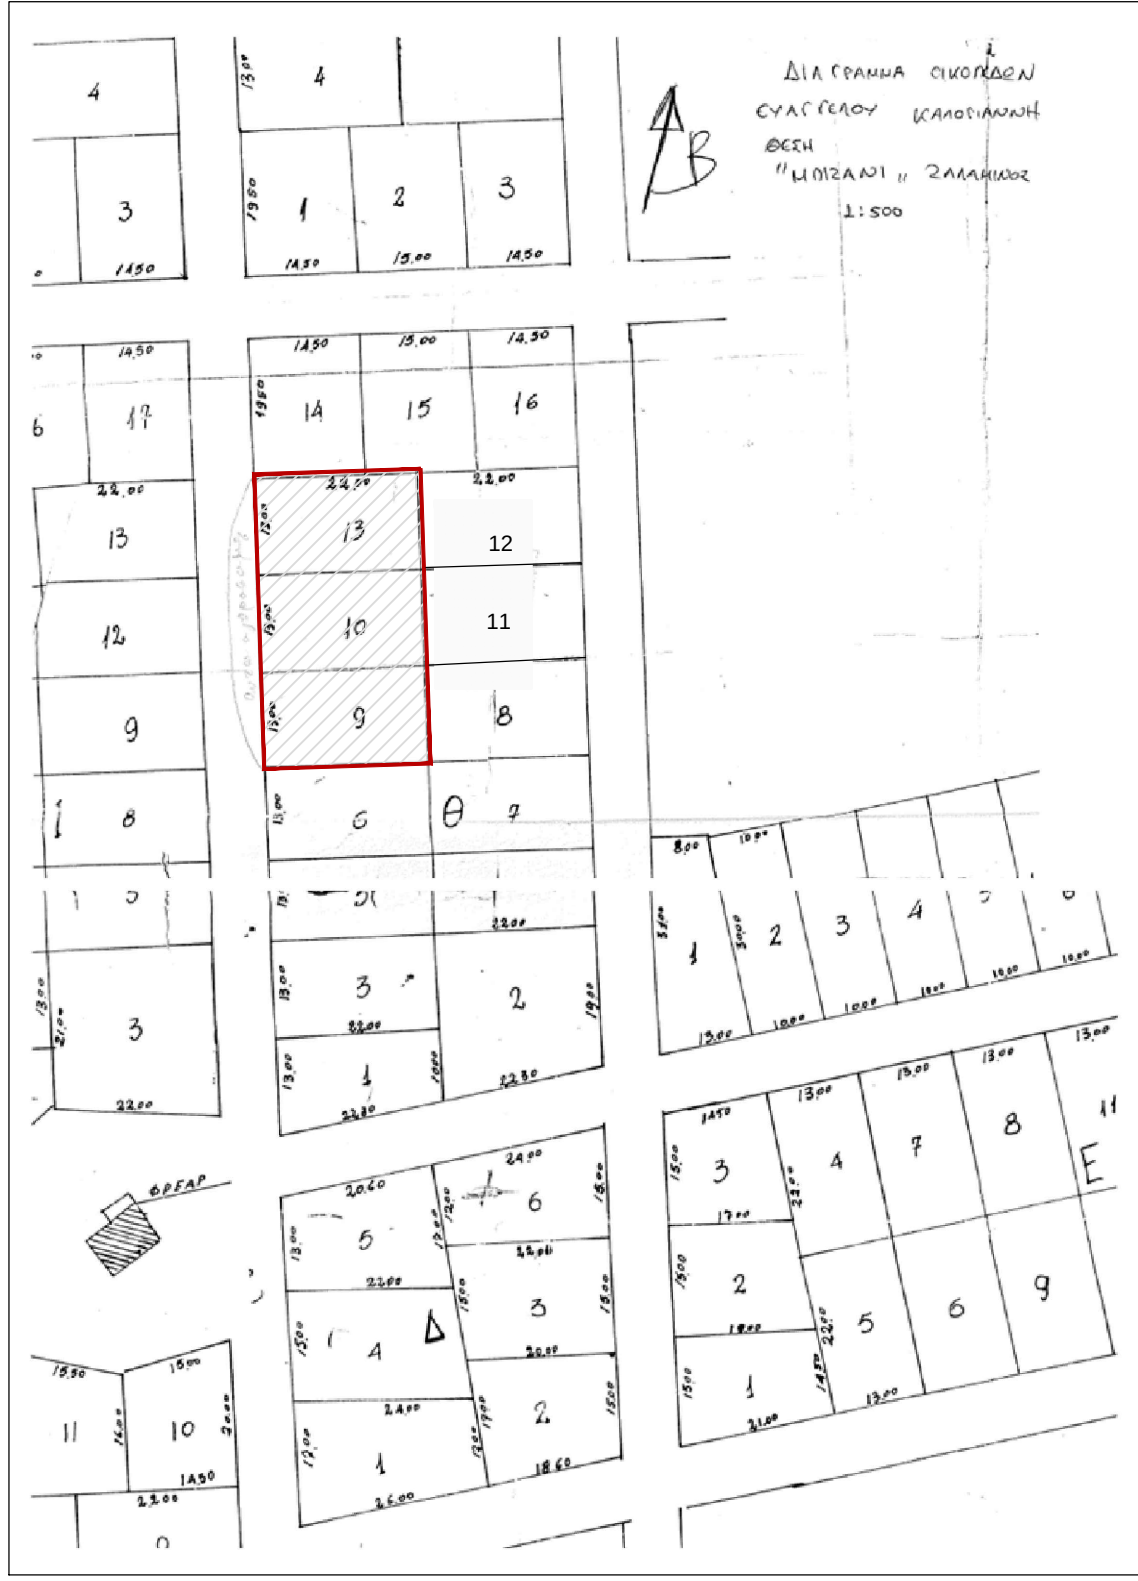



ΑΠΟΣΠΑΣΜΑ ΔΙΑΝΟΜΗΣ



ΑΠΟΣΠΑΣΜΑ ΟΡΘΟΦΩΤΟΧΑΡΤΗ ΕΘΝΙΚΟΥ ΚΤΗΜΑΤΟΛΟΓΙΟΥ
1 : 1000



ΑΠΟΣΠΑΣΜΑ ΔΑΣΙΚΩΝ ΧΑΡΤΩΝ

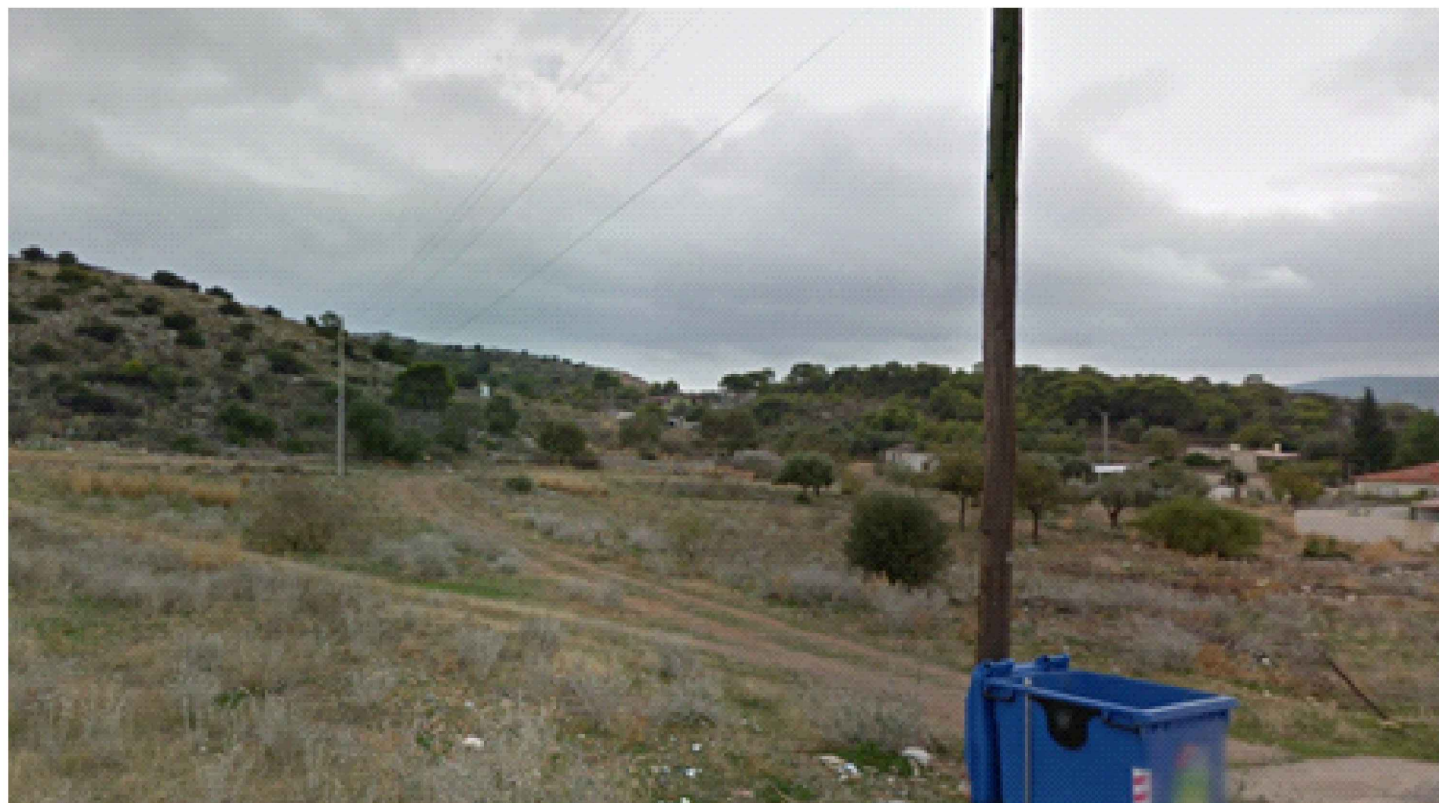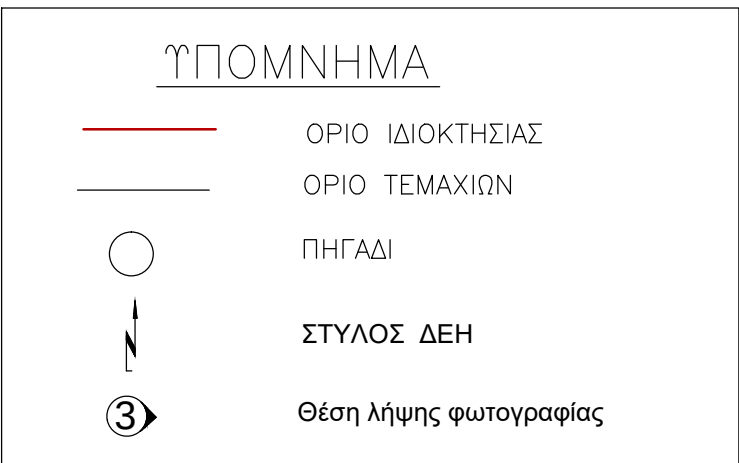

ΦΩΤΟΓΡΑΦΙΑ ΑΠΟ ΘΕΣΗ ΛΗΨΗΣ 3



ΦΩΤΟΓΡΑΦΙΑ ΑΠΟ ΘΕΣΗ ΛΗΨΗΣ 2



ΦΩΤΟΓΡΑΦΙΑ ΑΠΟ ΘΕΣΗ ΛΗΨΗΣ 1



- Ε1 ΔΕΝ ΕΜΠΙΠΤΕΙ ΣΤΙΣ ΔΙΑΤΑΞΕΙΣ ΤΗΣ ΔΑΣΙΚΗΣ ΝΟΜΟΘΕΣΙΑΣ (ΑΑ)
Ε2 ΕΜΠΙΠΤΕΙ ΣΤΙΣ ΔΙΑΤΑΞΕΙΣ ΤΗΣ ΔΑΣΙΚΗΣ ΝΟΜΟΘΕΣΙΑΣ (ΔΔ)
Ε3 ΕΜΠΙΠΤΕΙ ΣΤΙΣ ΔΙΑΤΑΞΕΙΣ ΤΗΣ ΔΑΣΙΚΗΣ ΝΟΜΟΘΕΣΙΑΣ (ΔΔ)

ΤΟΠΟΓΡΑΦΙΚΟ ΔΙΑΓΡΑΜΜΑ
ΚΛΙΜΑΚΑ : 1 : 200

ΣΤΟΙΧΕΙΑ ΠΡΟΒΟΛΙΚΟΥ ΣΥΣΤΗΜΑΤΟΣ
Προβολικό σύστημα : **Ελληνικό Γεωδαιτικό Σύστημα Αναφοράς '87 (ΕΓΣΑ '87)**
Ελλειψοειδές αναφοράς : GRS '80
Μεγάλος ημιάξονας ελλειψοειδούς (α) : 6378137.000m
Επιπλάτωση ελλειψοειδούς (1/f) : 1 / 298,257222101
Συντελεστής κλίμακας (Κο) : 0,9996

ΣΤΟΙΧΕΙΑ ΗΛΕΚΤΡΟΝΙΚΗΣ ΥΠΟΒΟΛΗΣ (άρθρο 3, παρ.4 Υ.Α. 27623/1752/ΘΕΚ 22168/14-6-2018)
Το παρόν διάγραμμα υποβλήθηκε ηλεκτρονικά στον ψηφιακό Υποδοχέα του ΝΠΔΔ "Ελληνικό Κτηματολόγιο" και έλαβε μοναδικό κωδικό ηλεκτρονικού διαγράμματος (ΚΗΔ) 2964429 / 03-05-2025

ΟΡΟΙ ΔΟΜΗΣΗΣ

ΕΚΤΟΣ ΣΧΕΔΙΟΥ
Π.Δ. 6-10-1978 (ΦΕΚ 538Δ/17-10-1978) - Τροπ. Π.Δ. 24-5-1985(ΦΕΚ 270Δ/31-5-1985), Ν. 3212/Π.Δ. 24-12-2003, (ΦΕΚ 308Α/31-12-2003)
- Ελάχιστα Όρια
I. Όλα τα τεμάχια με Ε= 4000τ.μ. και πρόσωπο 25μ. σε κοινόχρηστο δρόμο ή ρύθμιση που αφορά το ελάχιστο πρόσωπο δεν είναι για την ανέγερση κτίριων των αριθ. 2 x 3 φέρων εξοπλισμένα από δοσικούς ή αεριοκούς δρόμους και αρειθμικά καταρτισμένα τα εντός περιόριστων και η επιβολή του προσώπου δεν ισχύει για τα γήπεδα που προέρχονται του Ν.3212/03)
II. Τα τεμάχια που έχουν πρόσωπο επί Διεθνών, Εθνικών, Επαρχικών, Δημοτικών και κοινοτικών οδών όταν: Ε= 4000τ.μ.
Π= 45μ. Β=50μ.
Παρέκκλιση: I. Όσα βρίσκονται εντός ζώνης πόλεων, κυριών και οικισμών και είχαν >2000τ.μ. στις 24-4-77 ημέρα δημοσίευσης του ΠΔ/5-4-77(ΦΕΚ 133Δ)
II. α. Ε= 750τ.μ. Π= 10μ. Β=15μ. (προ 22.11.62/ΦΕΚ 142Δ)
β. Ε= 1200τ.μ. Π= 20μ. Β=35μ. (προ 12.9.64/ΦΕΚ 141Δ)
γ. Ε= 2000τ.μ. Π= 25μ. Β=40μ. (προ 17.10.78/ΦΕΚ 538Δ)
- Απόσταση από όριο >15μ.
Παρέκκλιση: 27.5μ. για γήπεδα τουλάχιστο 4000τ.μ. πρό της 15.4.81/ (ΦΕΚ 209Δ με πλάτος κτίριου <10μ.)
>2.5μ. με Π<20μ. και Β<35μ. για την α. περίπτωση
>5.0μ. με Π<45μ. και Β<50μ. για τις β. και γ. περιπτώσεις
- Ποσοστό Κάλυψης: 10%- Συντελεστής δόμησης: 0.2
- Όροι: Διο(2)- Ύψος: 7.50μ. (1.2μ. στήλη)

Το παρόν Τοπογραφικό Διάγραμμα είναι εξαρτημένο από το Κρατικό Σύστημα Συντεταγμένων Ε.Γ.Σ.Α. '87. Η εξέταση έγινε με χρήση δορυφορικού δέκτη GPS, μέσω του Ελληνικού Συστήματος Εντοπισμού ΗΕ.ΡΟ.Σ. Οι διαστάσεις και το εμβαδόν γεωτεμαχίου προέκυψαν αναλυτικά με βάση τις συντεταγμένες των σημείων.

ΕΜΒΑΔΟΝ ΓΕΩΤΕΜΑΧΙΟΥ: Ε_{Α,Β,Γ,Δ,Α} = 858,00 τ.μ.

ΣΥΝΤΕΤΑΓΜΕΝΕΣ ΚΟΡΥΦΕΣ ΓΕΩΤΕΜΑΧΙΟΥ - ΕΓΣΑ '87			
A/A	X	Y	
A	457583.43	4202729.96	22.00
B	457584.55	4202741.26	39.00
Γ	457584.58	4202774.72	22.00
Δ	457603.47	4202763.43	39.00
A	457583.43	4202729.96	

ΠΑΡΑΤΗΡΗΣΕΙΣ :

1. Το διάγραμμα είναι ενταγμένο στο κρατικό σύστημα συντεταγμένων Ε.Γ.Σ.Α. '87.
2. Οι διαστάσεις και το εμβαδόν υπολογίστηκαν αναλυτικά από τις συντεταγμένες των κορυφών.
3. Η αποτίμηση έγινε με την μέθοδο των πολικών συντεταγμένων με χρήση του ολοκληρωμένου γεωδαιτικού σταθμού Topcon GTS226
4. Η εξέταση από το ΕΓΣΑ'87 πραγματοποιήθηκε με σύστημα GPS, κάνοντας χρήση του Ελληνικού Συστήματος Εντοπισμού - ΗΕΡΟ.Σ. Χρησιμοποιήθηκε GPS δέκτης συχνότητας Sinox S8 GNSS.
5. Το εμβαδό του κτίριου αναφέρεται σε σχέση με την κάλυψη αυτού στο οικόπεδο.

ΥΠΟΜΝΗΜΑ

ΔΗΛΩΣΗ ΜΗΧΑΝΙΚΟΥ (Ν.651/1977)

Δηλώνω ότι σύμφωνα με το νόμο 651/77, για το γεωτεμάχιο " Α-Β-Γ-Δ-Α " με εμβαδόν 858.00 m², που βρίσκεται στη θέση " Μπιζάνι ", του Δήμου Σαλαμίνας, Περιφέρειας Αττικής :

- α) Είναι Εκτός Σχεδίου Δόμησης,
β) Βρίσκεται εκτός ρυμοτομικού σχεδίου.
γ) Εντός αυτού δεν διέρχονται εναέριες γραμμές μεταφοράς υψηλής τάσης της ΔΕΗ.
δ) Εντός αυτού δεν διέρχεται αγωγός φυσικού αερίου.
ε) Εντός αυτού ή σε απόσταση μικρότερη των 20 m από αυτό, δεν διέρχεται ρέμα.

ΔΗΛΩΣΗ ΥΠΟΠΟΙΗΣΗΣ ΟΡΙΩΝ

Τα όρια του γεωτεμαχίου με στοιχεία " Α-Β-Γ-Δ-Α ", έχουν ληφθεί με βάση υποδείξει του ιδιοκτήτη.

ΔΗΛΩΣΗ ΜΗΧΑΝΙΚΟΥ (Ν.1337/1983)

Δηλώνω ότι το γεωτεμάχιο που εμφανίζεται στο τοπογραφικό διάγραμμα με στοιχεία " Α-Β-Γ-Δ-Α ", βρίσκεται εκτός σχεδίου δόμησης. Έως την έναρξη στο σχέδιο, το γεωτεμάχιο δεν εμπίπτει στις διατάξεις του νόμου 1337/83 και δεν είναι υπόχρεο εισφοράς σε γη και χρήμα.

ΔΗΛΩΣΗ ΜΗΧΑΝΙΚΟΥ (Ν.2308/1995)

Το γεωτεμάχιο που εμφανίζεται στο τοπογραφικό διάγραμμα με στοιχεία " Α-Β-Γ-Δ-Α ", βρίσκεται σε περιοχή που έχει ενταχθεί στο Εθνικό Κτηματολόγιο και έχει ΚΑΕΚ 051292124009/0/0 .

ΔΗΛΩΣΗ παρ. 4 του άρθρου 142 του Ν. 4483/2017

Δηλώνω εν' γνώση του νόμου, για το γεωτεμάχιο με στοιχεία "Α,Β,Γ,Δ,Α" και εμβαδόν 858,00 τ.μ., που απεικονίζεται στο παρόν Τοπογραφικό διάγραμμα, σύμφωνα με τους δασικούς χάρτες που αναρτήθηκαν υπ' αριθμ. ΦΕΚ 819Δ/2022 - Κύρωση του δασικού χάρτη Σαλαμίνας, περιφερειακής ενότητας Νήσων, - το τμήμα Ε1, εμβαδού 35,68 τμ. ΔΕΝ εμπίπτει στις δασικές εν' γένει εκτάσεις, φέρει χαρακτηρισμό (ΑΑ), - το τμήμα Ε2, εμβαδού 817,88 τμ. εμπίπτει στις δασικές εν' γένει εκτάσεις, φέρει τον χαρακτηρισμό (ΔΔ), - το τμήμα Ε3, εμβαδού 4,44 τμ. εμπίπτει στις δασικές εν' γένει εκτάσεις, φέρει τον χαρακτηρισμό (ΔΑ).

Ο ΜΗΧΑΝΙΚΟΣ

ΔΗΛΩΣΗ ΙΔΙΟΚΤΗΤΗ (Ν.4030/2011)

Οι κάτωθι υπογεγραμμένοι, δηλώνουμε ότι :

Τα αρχικά και υποσημειωμένα όρια του γεωτεμαχίου με στοιχεία "Α,Β,Γ,Δ,Α", εμβαδού Ε= 858,00 τ.μ. που βρίσκεται στην περιοχή "Μπιζάνι" Σαλαμίνας - εκτός σχεδίου, έχουν υποδεχτεί από εμάς και ευθυνόμενα για την ακρίβεια αυτών.

Οι Δηλούντες
Αλίκη Προυσαέως

ΕΡΓΟ :	
ΤΟΠΟΓΡΑΦΙΚΟ ΔΙΑΓΡΑΜΜΑ ΓΕΩΤΕΜΑΧΙΟΥ	
ΙΔΙΟΚΤΗΣΙΑ :	
ΑΛΙΚΗ ΠΡΟΥΣΑΕΩΣ Κληρονόμοι Ν. ΠΡΟΥΣΑΕΩΣ	
ΘΕΣΗ :	
ΕΚΤΟΣ ΣΧΕΔΙΟΥ, ΠΕΡΙΟΧΗ " ΜΠΙΖΑΝΙ " ΔΗΜΟΣ ΣΑΛΑΜΙΝΑΣ ΠΕΡΙΦΕΡΕΙΑ ΑΤΤΙΚΗΣ	
ΜΕΛΕΤΗΤΗΣ :	
ΕΛΕΝΗ ΖΥΓΟΥΡΗ ΠΟΛΙΤΙΚΟΣ ΜΗΧΑΝΙΚΟΣ MSc	
ΘΕΜΑ ΣΧΕΔΙΟΥ :	ΑΡΙΘΜΟΣ ΣΧΕΔΙΟΥ
ΤΟΠΟΓΡΑΦΙΚΟ ΔΙΑΓΡΑΜΜΑ	A 1
ΚΛΙΜΑΚΑ 1 : 200	
ΣΦΡΑΓΙΔΑ - ΥΠΟΓΡΑΦΗ :	
ΕΛΕΝΗ Ζ. ΖΥΓΟΥΡΗ ΔΙΠΛ. ΠΟΛΙΤΙΚΟΣ ΜΗΧΑΝΙΚΟΣ MSc ΑΡΙΘΜΟΣ ΕΠΙΤΥΓΟΥ ΤΩΝ ΚΑΔΕΣ ΣΥΝΑΝΤ. 35 ΑΓ. ΠΑΡΑΚΛΕΤΗ 193-43 ΑΒΗΒΑΒΕΛ7851 - ΔΟΥ ΚΟΛΑΡΓΟΥ	
ΕΛΕΝΗ ΖΥΓΟΥΡΗ 07.05.2025 14:55	
ΗΜΕΡΟΜΗΝΙΑ : ΑΠΡΙΛΙΟΣ 2025	